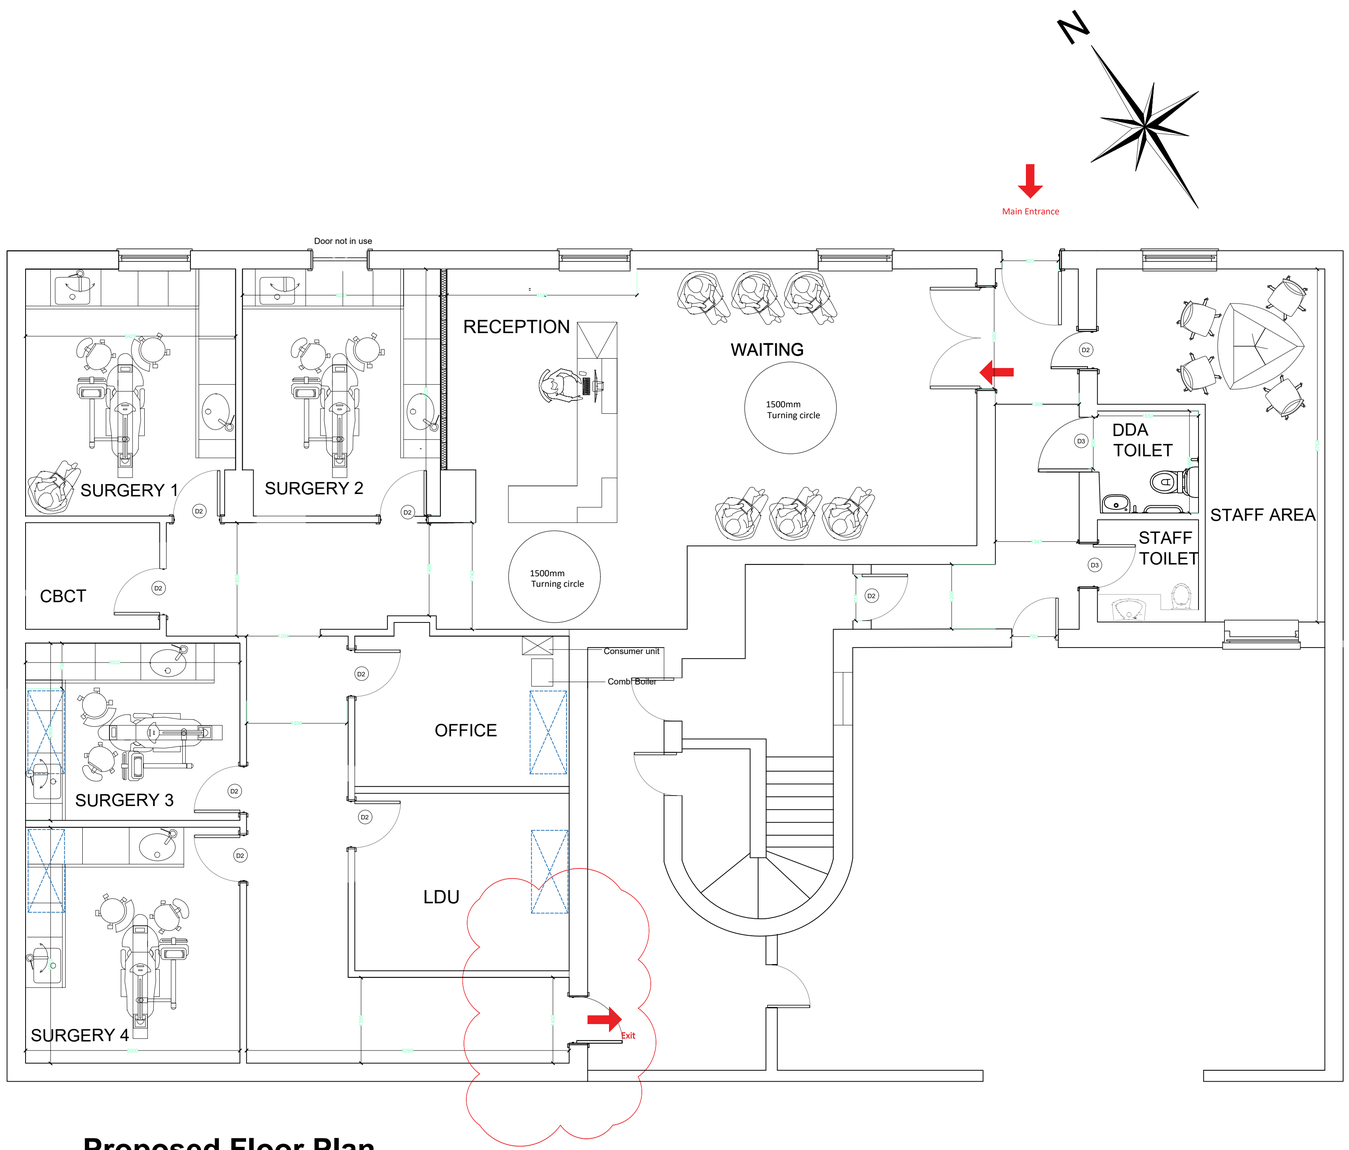


Proposed Floor Plan

Scale 1:50

PROPOSED FLOOR PLAN – OPERATIONAL & ACCESSIBILITY NOTE:

This drawing illustrates the proposed internal layout and furniture arrangement for the dental practice, showing functional relationships between clinical and non-clinical spaces to support safe and efficient operation.

Each dental surgery is arranged to include:

One dental chair

Two clinical sinks (clinical handwash + utility/instrument sink)

The LDU (Local Decontamination Unit) is provided with two sinks to support clean/dirty workflow separation.

The reception and waiting area is arranged as an open-plan layout, providing clear visibility, circulation, and patient flow.

The entire floor plan has been designed to be fully accessible to wheelchair users, with compliant circulation widths, door clearances, manoeuvring spaces, and accessible sanitary facilities, in accordance with Standards 4.1 and 4.2 (access to and within buildings) of the Scottish Technical Handbook (Non-Domestic) Technical Handbook.

Surgeries, WCs and LDU are finished with Polyflor Forest FX PUR vinyl flooring. Reception, waiting area and corridors are finished with commercial carpet tiles. All floor finishes provide uniform, stable, slip-resistant surfaces suitable for circulation and wheelchair access in accordance with the Scottish Technical Handbook.

Accessibility & Inclusive Design

The layout has been designed in accordance with the Scottish **Building Standards Technical Handbook (Non-Domestic) to provide an inclusive and accessible environment.**

Key measures include:

- Step-free access to all public areas
- Compliant corridor widths and door clear openings
- Wheelchair manoeuvring space provided throughout
- Accessible WC
- Reception desk with a lowered accessible counter section
- Open-plan waiting area allowing wheelchair seating
- Floor finishes selected to provide uniform, slip-resistant surfaces

All routes, facilities, and fittings are suitable for wheelchair users and those with reduced mobility.

SCALE BAR: 1:50

0 1 2 3 4 5m

IMPORTANT NOTES

INFECTION CONTROL
This design must be approved by the appointed Infection Control Advisor prior to commencement of works.

BUILDING REGULATIONS COMPLIANCE
All works shall be carried out in full accordance with the current Building Regulations, applicable Codes of Practice, and relevant British Standards.

DIMENSIONS & SITE VERIFICATION

Work to figured dimensions only.

Do not scale from this drawing.

All dimensions must be checked on site prior to commencement of works.

Any discrepancies must be reported before construction proceeds.

COORDINATION OF DOCUMENTS
All information is to be read in conjunction with other relevant drawings, specifications, and reports associated with the project.

REV:	DRAWN BY:	DATE:	CHECKED BY:	DATE:	ISSUED BY:	DATE:
	Faizan Ali	07/04/26	Angbeen Najam	06/07/26	Angbeen Najam	06/07/26
02	Angbeen Najam	22/09/26	Angbeen Najam	22/09/26	Angbeen Najam	22/09/26

SCALES @ A1	ISSUING OFFICE	INTERNAL PROJECT No.
1:50		

STATUS	PURPOSE OF ISSUE
C1	CONSTRUCTION

PROJECT

Tolbooth st Kirkcaldy

DRAWING TITLE

PROPOSED
FLOOR PLAN

CLIENT

DRAWING NUMBER	REVISION
A-02	02
PROJ | ORIGIN | ZONE | LEVEL | FILETYPE | ROLE | NO	